


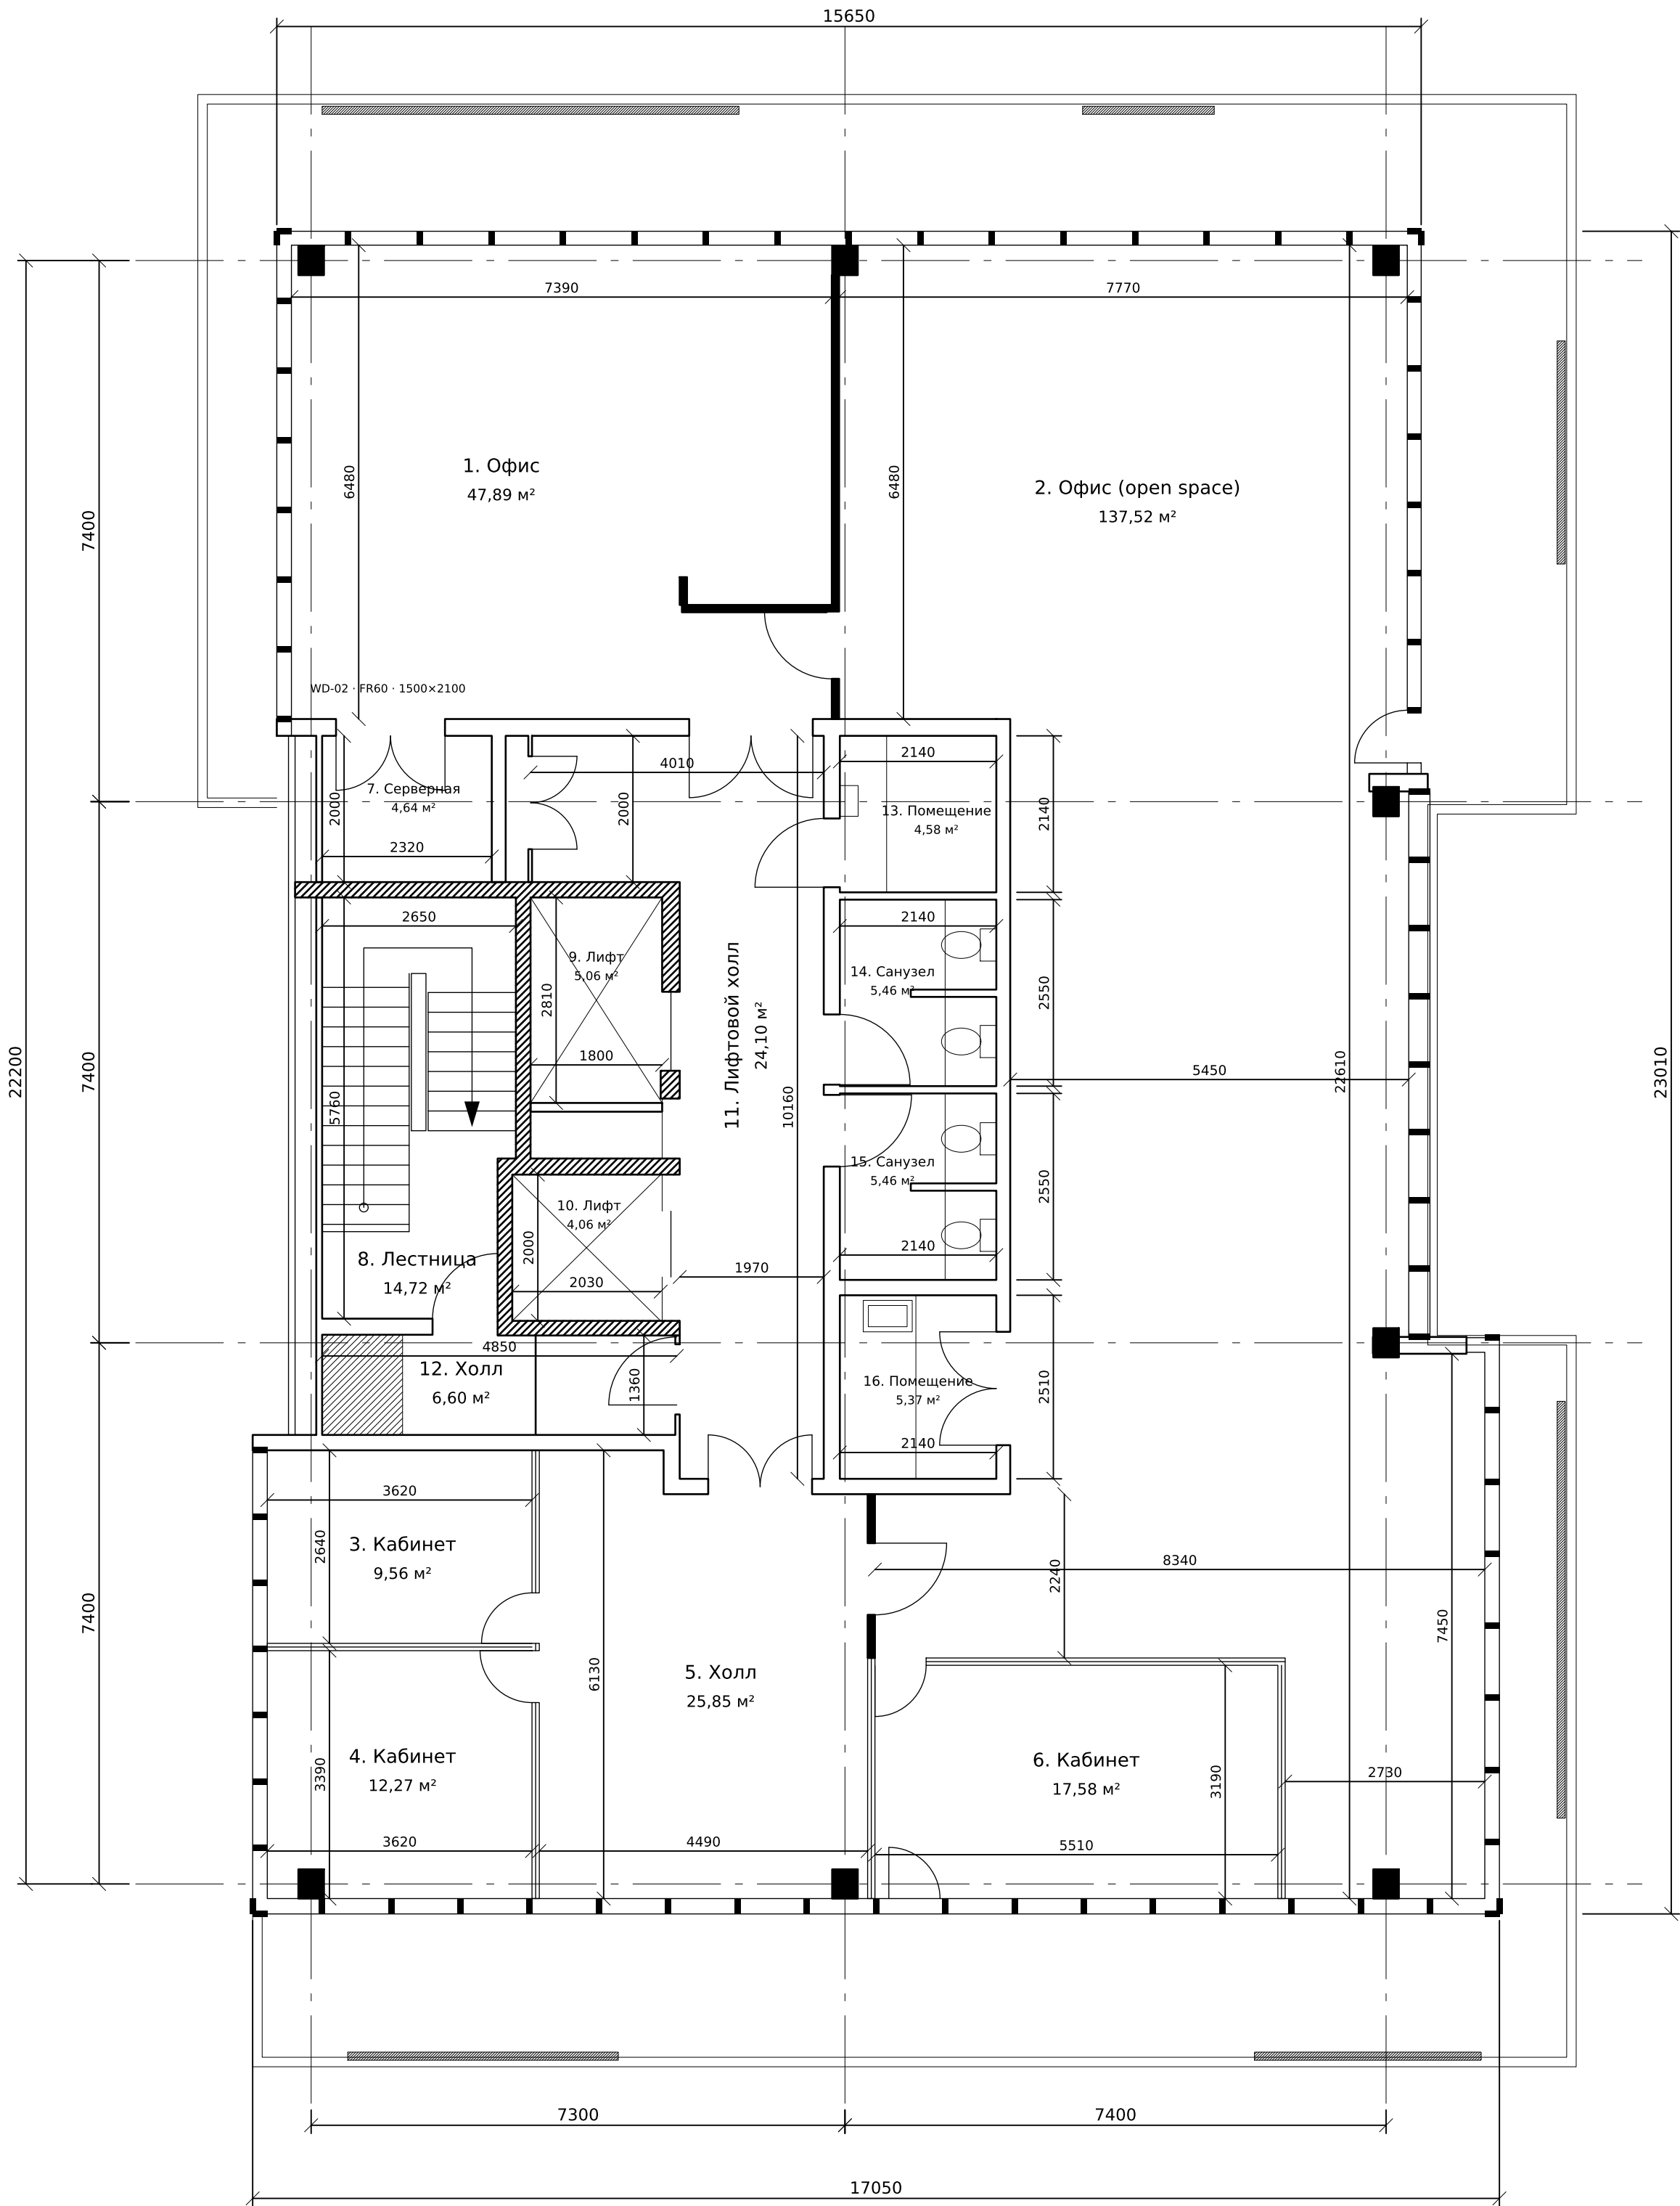

Экспликация помещений

№	Наименование	Размеры в свету, мм	Площадь, м²
1	Офис	7390 × 6480	47,89
2	Офис (open space)	сложной формы — см. план	137,52
3	Кабинет	3620 × 2640	9,56
4	Кабинет	3620 × 3390	12,27
5	Холл	4490 × 6130 (сложной формы)	25,85
6	Кабинет	5510 × 3190	17,58
7	Серверная	2320 × 2000	4,64
8	Лестница	2650 × 5760 (сложной формы)	14,72
9	Лифт	1800 × 2810	5,06
10	Лифт	2030 × 2000	4,06
11	Лифтовой холл	1970 × 10160 (сложной формы)	24,10
12	Холл	4850 × 1360	6,60
13	Помещение	2140 × 2140	4,58
14	Санузел	2140 × 2550	5,46
15	Санузел	2140 × 2550	5,46
16	Помещение	2140 × 2510	5,37
Итого			330,70

Условные обозначения

- железобетонные стены
- перегородки существующие
- перегородки новые
- перегородки стеклянные
- колонны 350×400
- витраж (навесной фасад)
- оси

Примечания

- Размеры помещений — в свету, между гранями стен и витража.
- Шаг осей по вертикали 7400 мм — по оригиналу; шаг по горизонтали (7300, 7400) и все размеры помещений определены по масштабу.
- Стены кабинетов 3, 4 и 6 — стеклянные перегородки.
- Маркеры разрезов/фасадов и марки дверей/окон не перенесены; сантехника и лестница показаны упрощённо.

План 1-го этажа (1ST FLOOR) — размеры помещений

Источник	изображение плана, перечерчено (ред. 2)
Масштаб	1:75 (лист А2); размеры в мм, площади в м²
Размеры	по масштабу; шаг осей 7400 мм — по оригиналу
Точность	±30 мм (разбор при увеличении ×3)